

PROJETO

CASA RICARDO

CLIENTE

Ricardo José Alves Nunes

LOCALIZAÇÃO

Rua Bernardo Marques, nº6 - Bloco C1, 1B
Santo António dos Cavaleiros - Loures

FASE

ANTEPROJETO

TIPO DE DESENHO

ESTUDOS DE LAYOUT

CÓDIGO DO PROJETO PROJ2026_285

ESCALA FORMATO

1/100 A3

DATA VERSÃO

09 / 07 / 2026 01

STATUS DO DOCUMENTO

PRELIMINAR

TECNICO/A RESPONSÁVEL

Rute Frias
OA N.º 16398

DESENHADO POR

Rute Frias
Arquiteta

APROVADO POR

Robson Senna
COO

HISTÓRICO DE REVISÕES


REV.	DATA	DESCRIÇÃO
01	09/07/2026	Proposta de layout

Nº DE FOLHA

ARQ - 03

TOTAL DE FOLHAS 03

Este desenho é propriedade da Senna Building e não poderá ser reproduzido, divulgado ou copiado, total ou parcialmente, sem autorização prévia e expressa por escrito.
Todas as dimensões, cotas e condições existentes indicadas neste desenho deverão ser verificadas e confirmadas em obra antes da execução dos trabalhos.

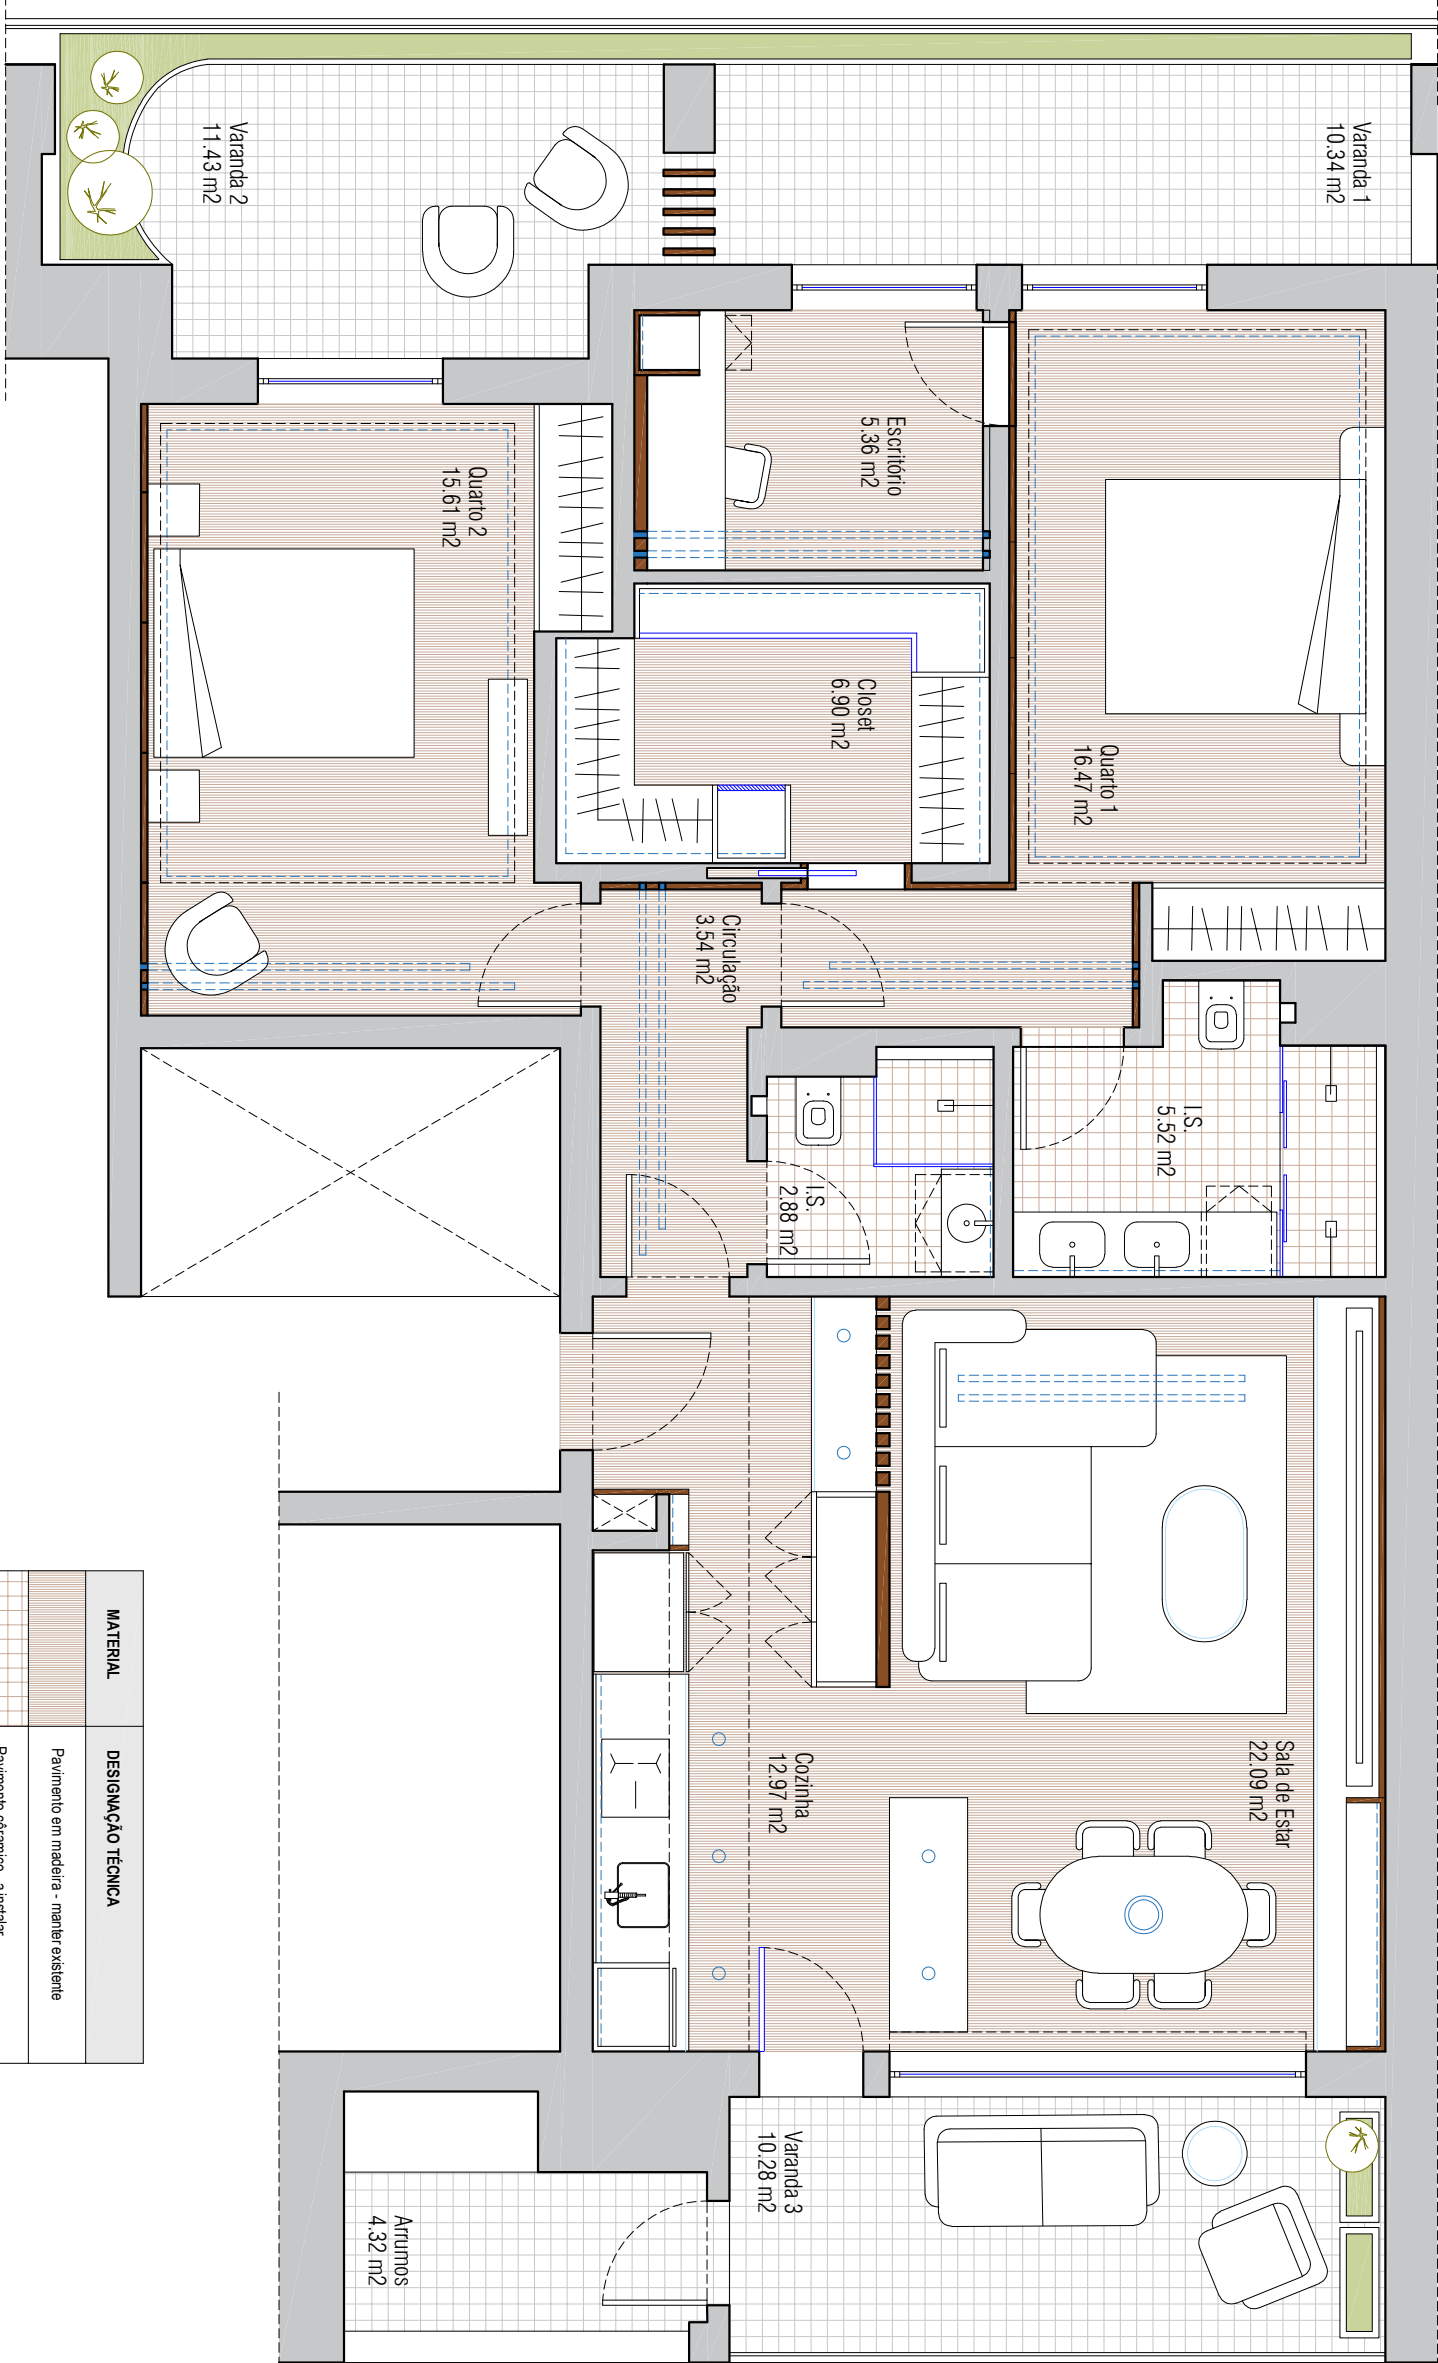

MATERIAL	DESIGNAÇÃO TÉCNICA
	Pavimento em madeira - manter existente
	Pavimento cerâmico - a instalar
	Pavimento cerâmico - a manter
	Fornas de madeira
	Illuminação linear de tecto e parede
	Illuminação em sanca
	Illuminação baixa de mobiliário
	Illuminação LED para mobiliário
	Candeiro de tecto
	Focos de tecto